


LAYOUT PLAN OF BISHOP JEROME INSTITUTE , KOLLAM

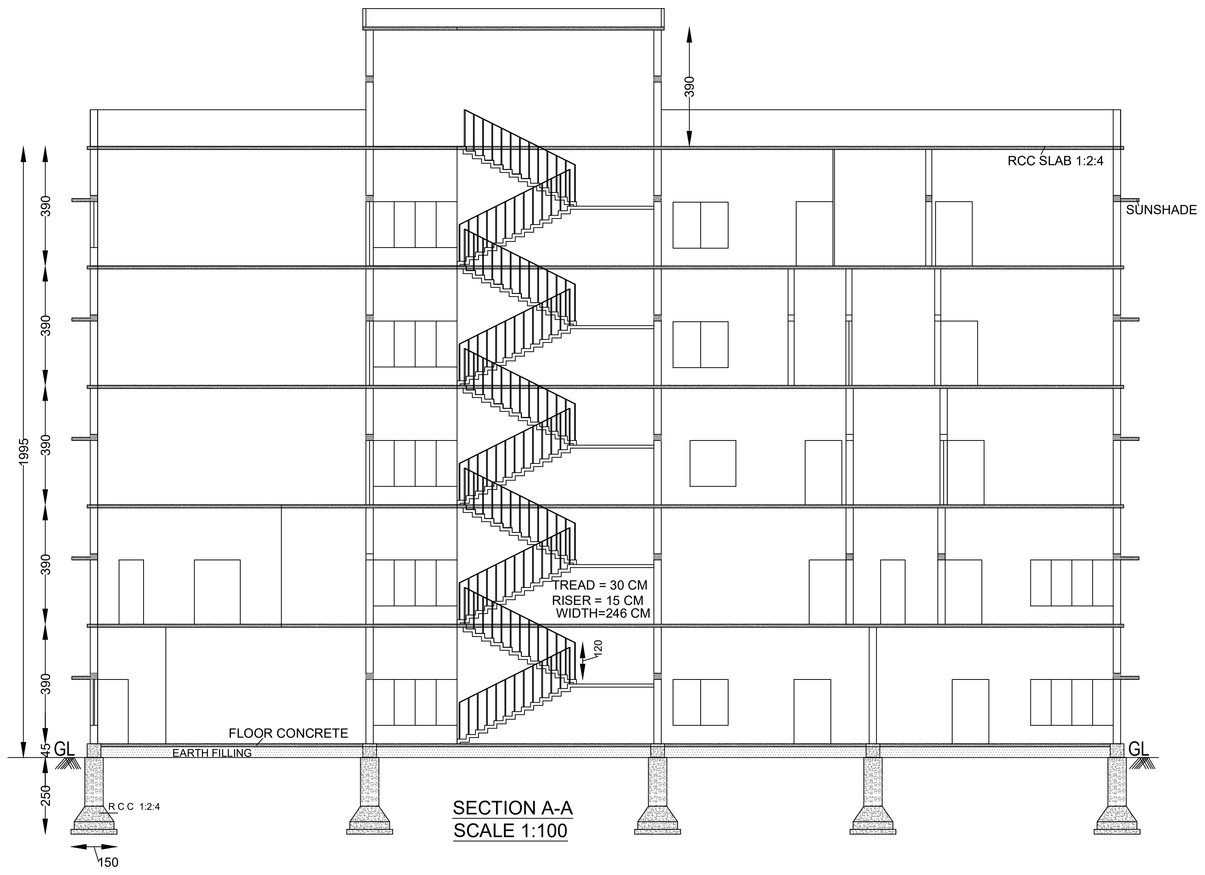

SECTION A-A
SCALE 1:100

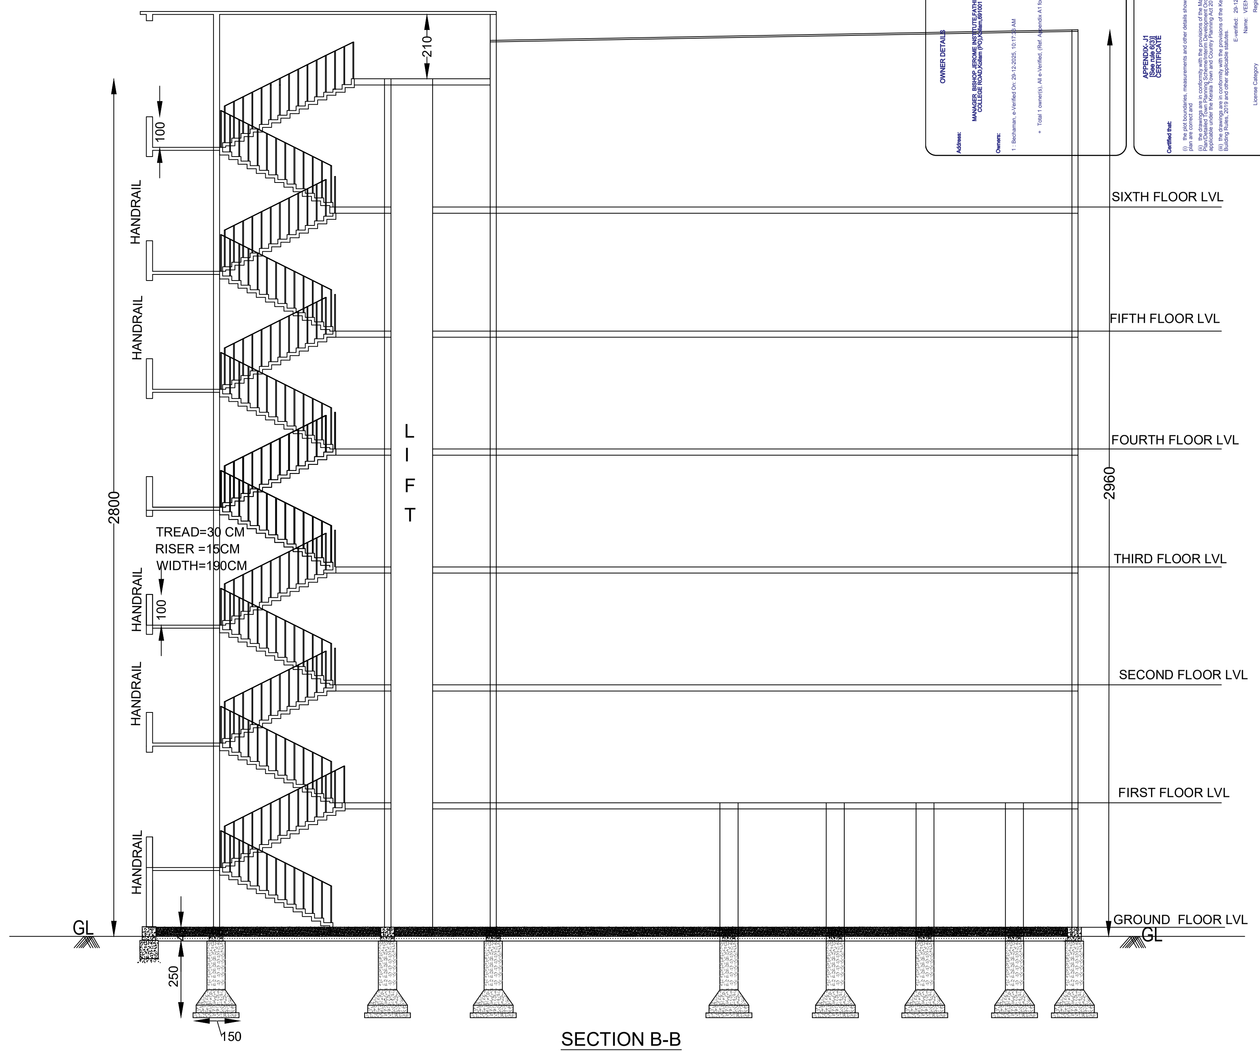

SECTION B-B
SCALE 1:100

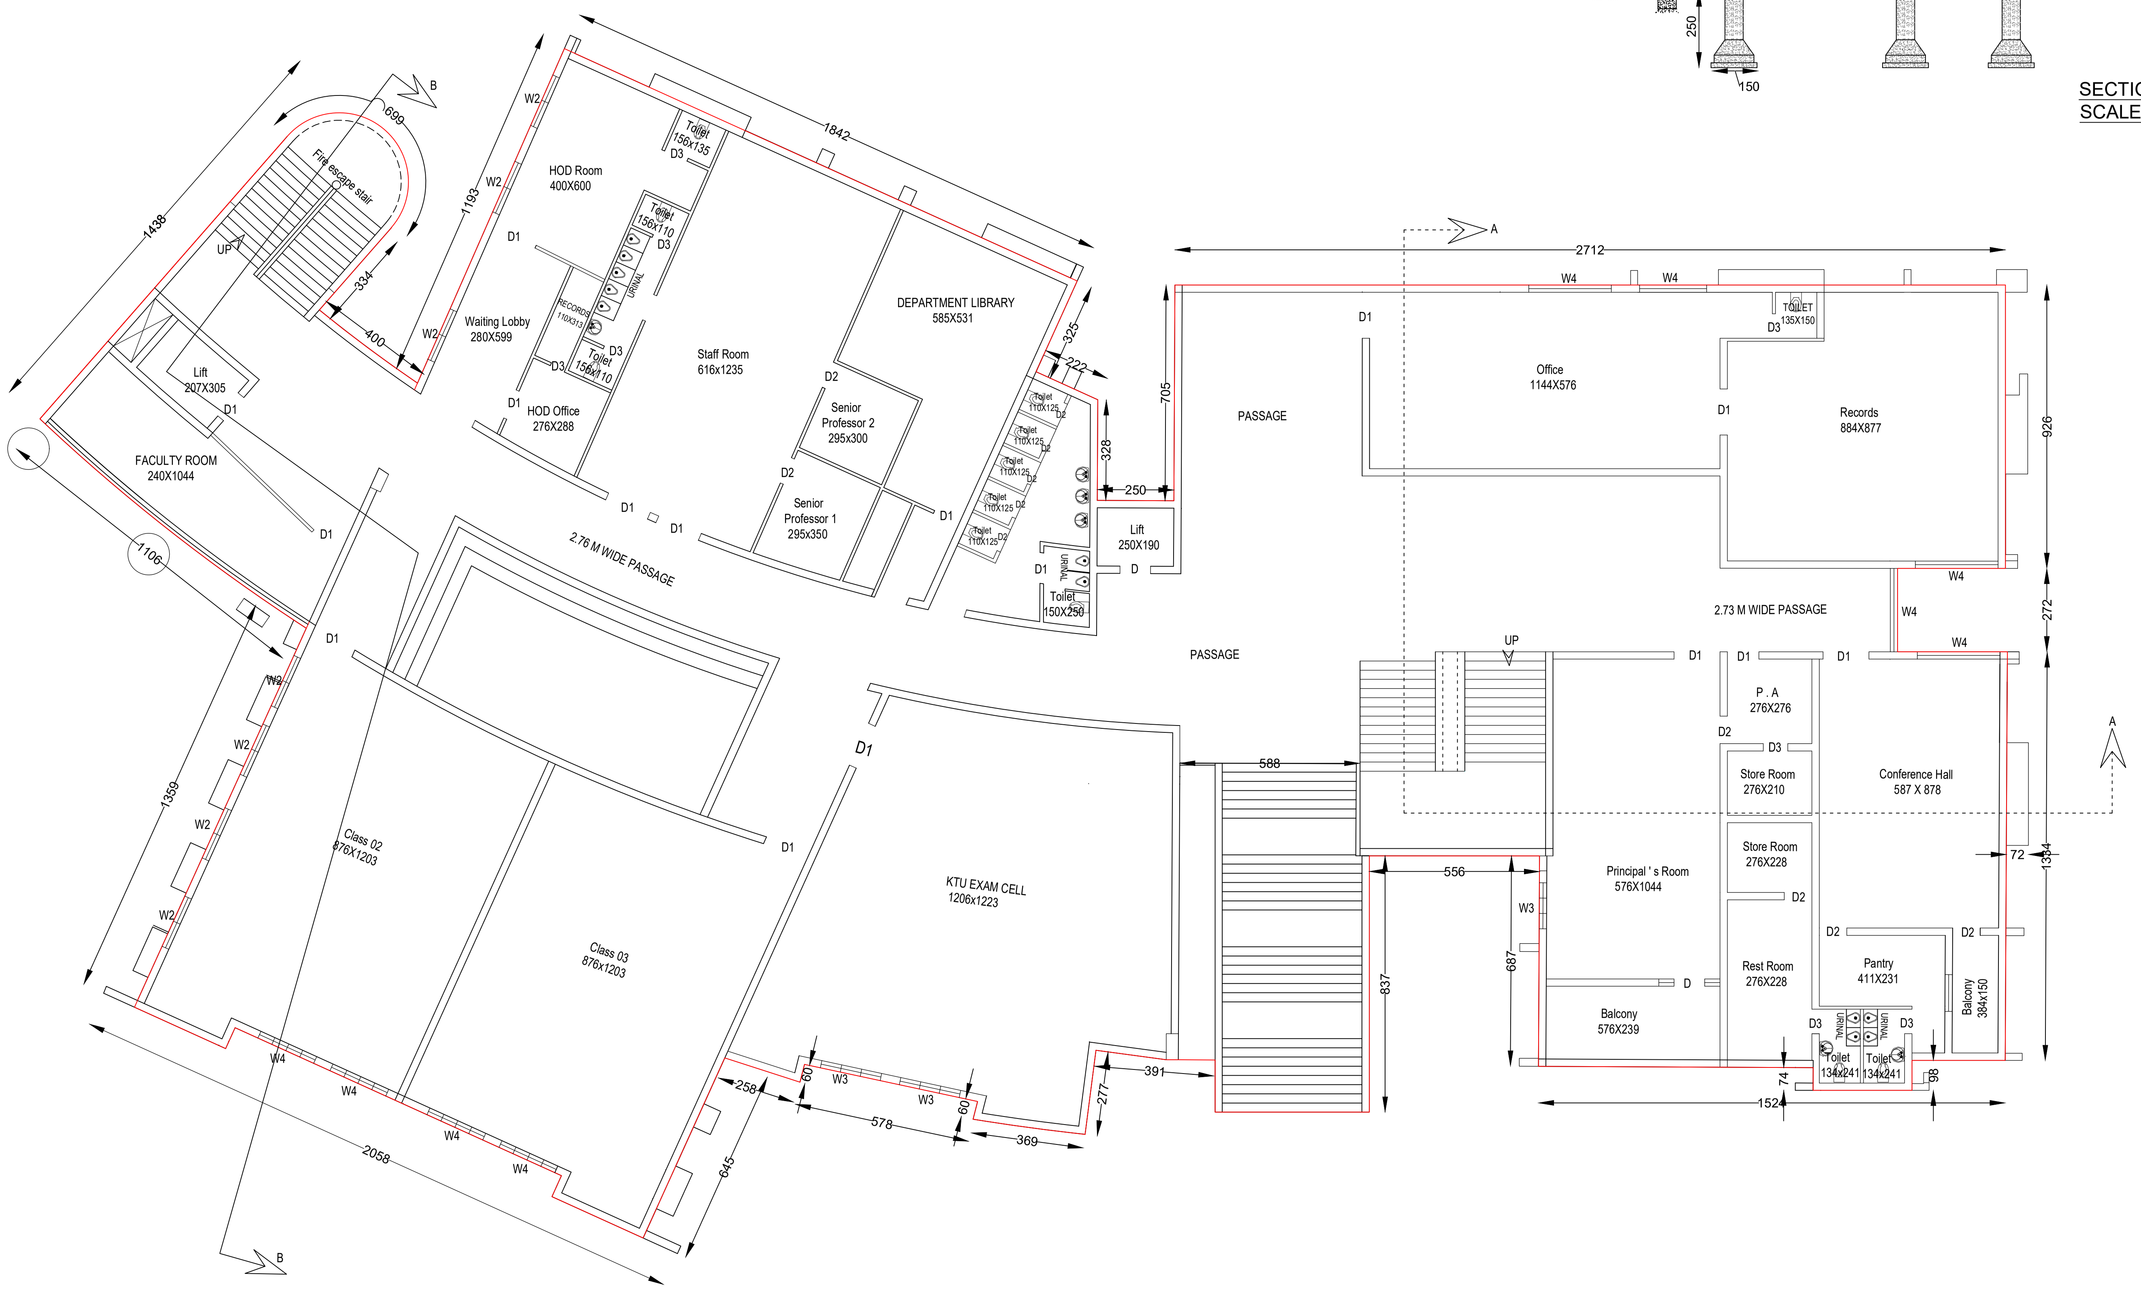

FIRST FLOOR PLAN

SANITATION CALCULATION	
1.MAIN BLOCK	
TOTAL FLOOR AREA =	8757.64 SQM
WATER CLOSET MALE =	1 PER EVERY 475 M2
	= 8757.64 / 475 = 18.44 NOS.
WATER CLOSET FEMALE =	1 PER EVERY 300 M2
	= 8757.64 / 300 = 29.19 NOS.
URINALS MALE	= 1 PER EVERY 600 M2
	= 8757.64 / 600 = 14.59 NOS.
SPECIAL URINALS / ADDITIONAL WC FOR FEMALE = 1 PER EVERY 600 M2	
	= 8757.64 / 600 = 14.59 NOS.
WASH BASIN MALE	= 1 PER EVERY 475 M2
	= 8757.64 / 475 = 18.44 NOS.
WASH BASIN FEMALE	= 1 PER EVERY 475 M2
	= 8757.64 / 475 = 18.44 NOS.

ALL DIMENSIONS ARE IN CM

EXTENSION PROPOSED PLAN OF EDUCATIONAL BUILDING

APPLICANT
MANAGER
Fr.BENJAMINE PALLIYAD, I.I.L.
BISHOP JEROME INSTITUTE
FATHIMA COLLEGE ROAD
KOLLAM-691001

SIGNATURE OF APPLICANT

DETAILS OF PLOT

DISTRICT	: KOLLAM
TALUK	:KOLLAM
VILLAGE	: VADAKKEVILA
CORPORATION	:KOLLAM
SY.NO	:13/2 1 Hr. 95 ARES
	: 14/2 3 Hr. 24 ARES
TOTAL	: 5 Hr. 19 ARES
WARD NO.	: 44

LICENCY CERTIFICATE

Certified that :

i) The plot boundaries, measurements and other details shown in the site plan are correct and
ii) The drawings are in conformity with the provisions of the master plan/detailed town planning scheme/interim development order as applicable under the Kerala Town and Country Planning Act 2016
iii) The drawings are in conformity with the provisions of the Kerala Municipality/Corporation building rules, 2019 and other applicable statutes

Certified that :

i) The document(s) in support of the ownership of the plot has/have been verified and that the applicant (s) has/have every right of construction in this plot;
ii) The plot boundaries,measurments and other details shown in the site plan have been verified at site and found correct and
iii) The drawings are in conformity with the provisions of the master plan/detailed town planning scheme/interim development order as applicable under the Kerala Town and Country Planning Act 2016
iv) The drawings are in conformity with the provisions of the Kerala Municipality/Corporation building rules, 2019 and other applicable statutes

SECRETARY

HABI®
HABI INDUSTRIAL CONSULTANCY PVT. LTD.
ARCHITECTURE-INTERIOR DESIGN
VISUALIZATION-PROJECT MANAGEMENT
Nedumpana, kollam-691576
email: habiindustrialconsultancy@gmail.com
mobile : 944 797 0389